



감정평가법인 정원 인테리어 제안서

INTERIOR PROPOSAL

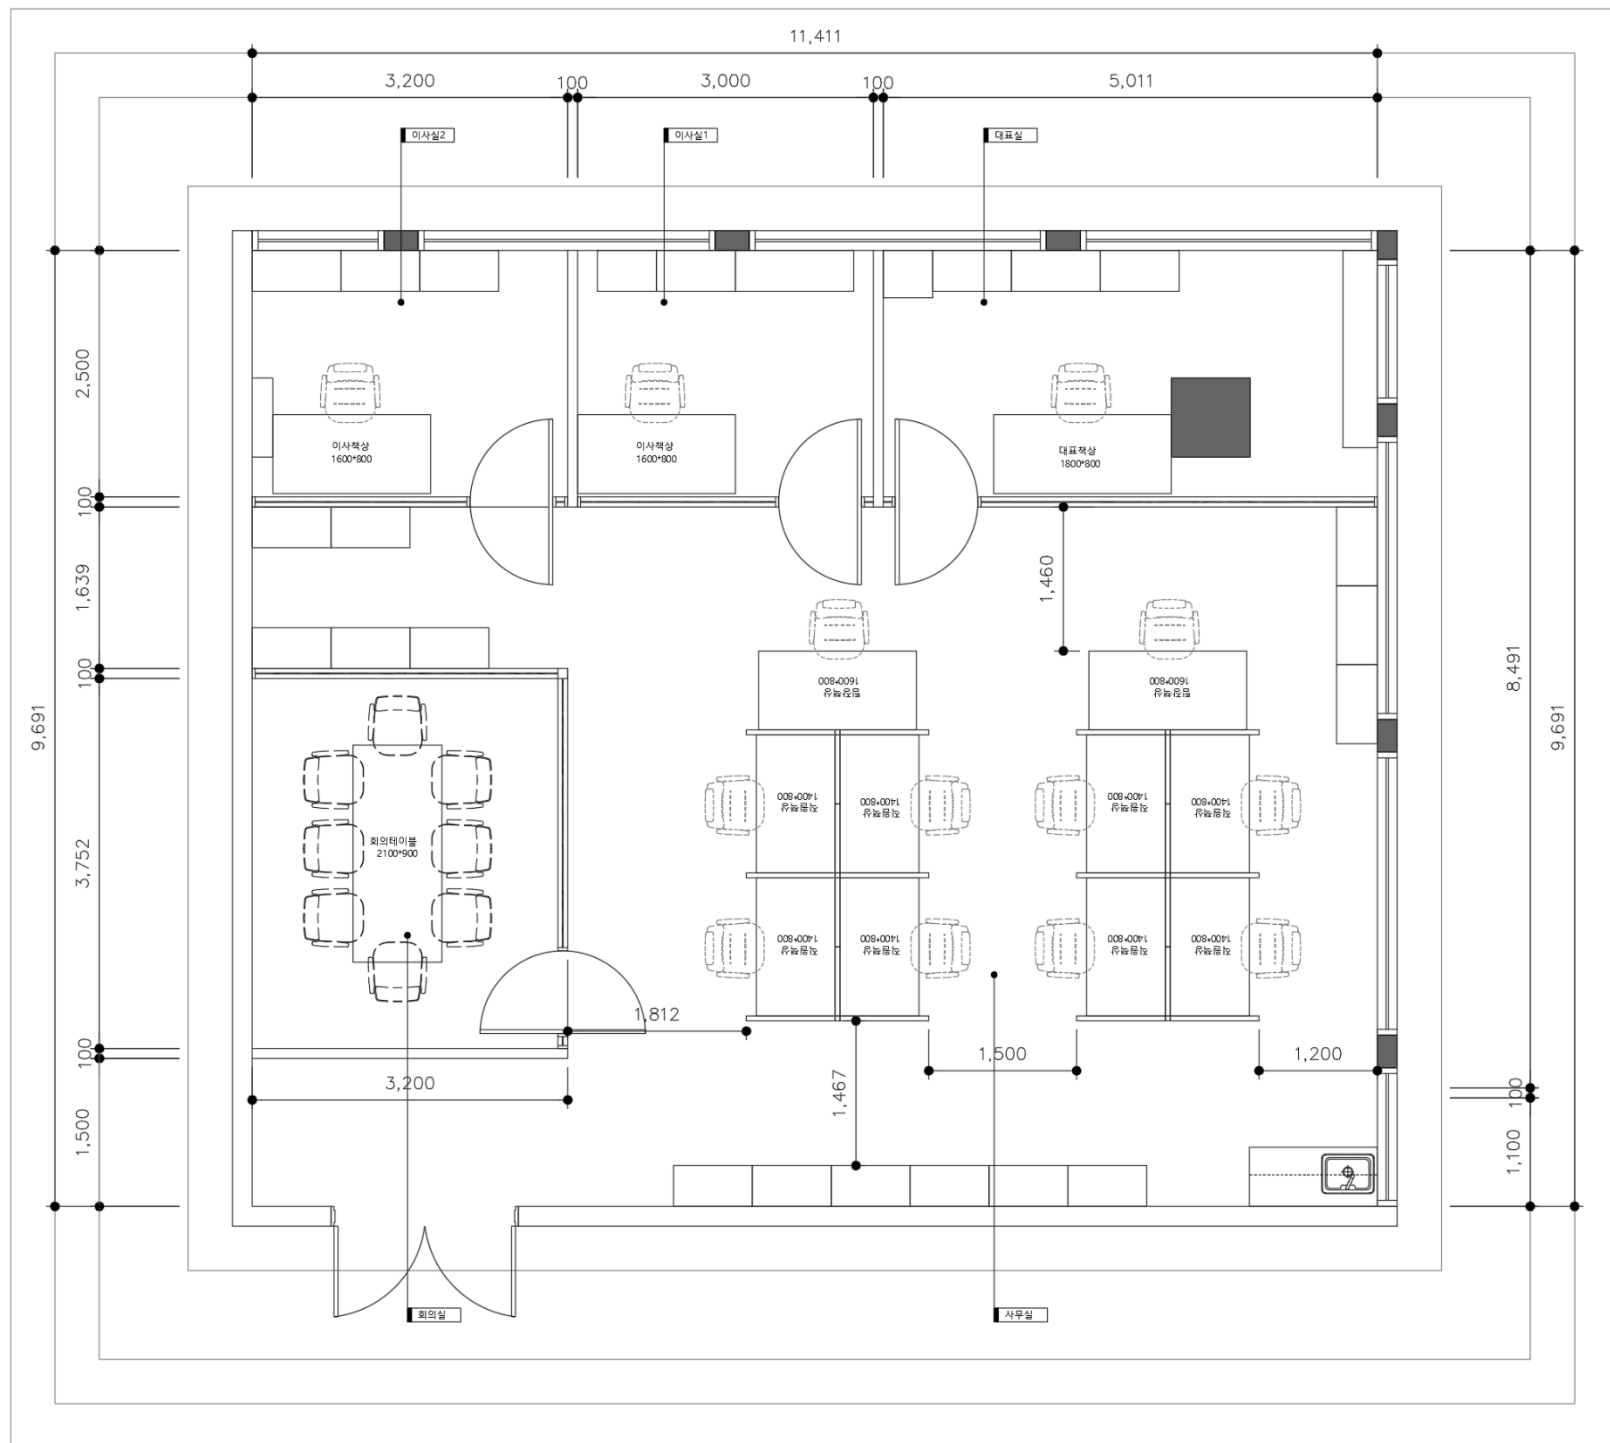

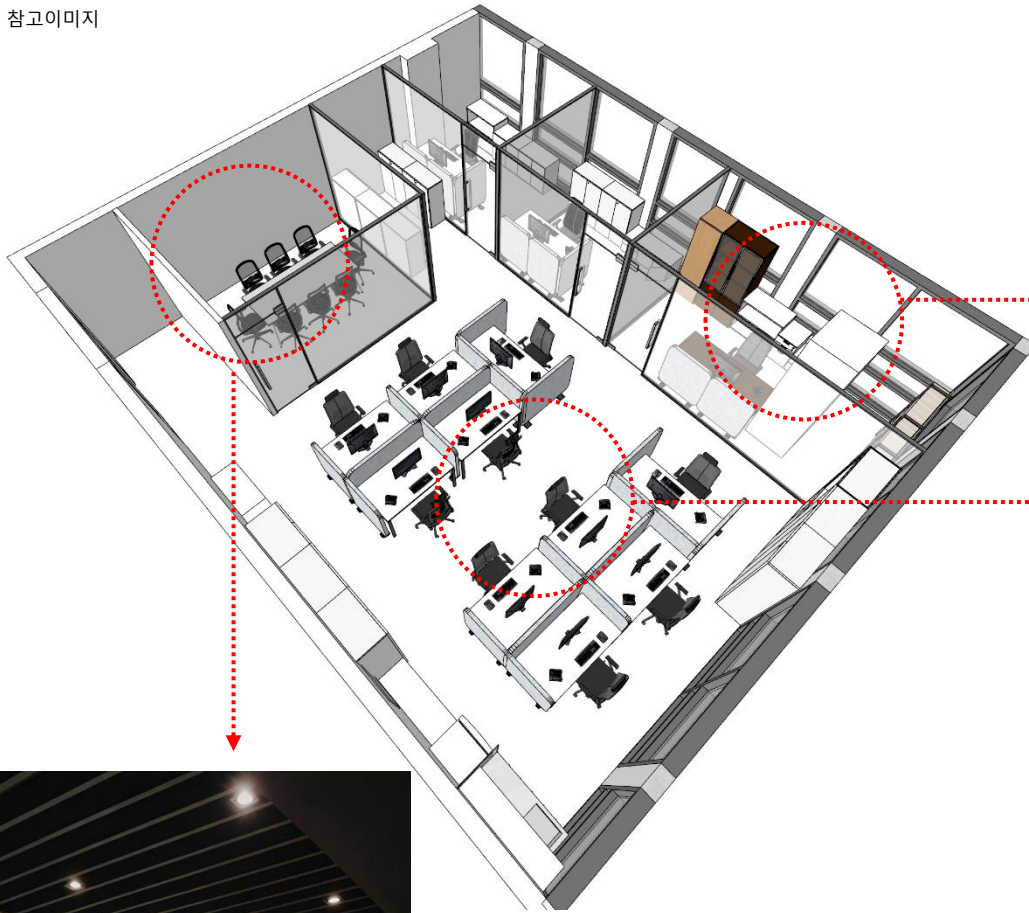

대표실 및 이사실



회의실





사무실



대표실 및 이사실

평면도

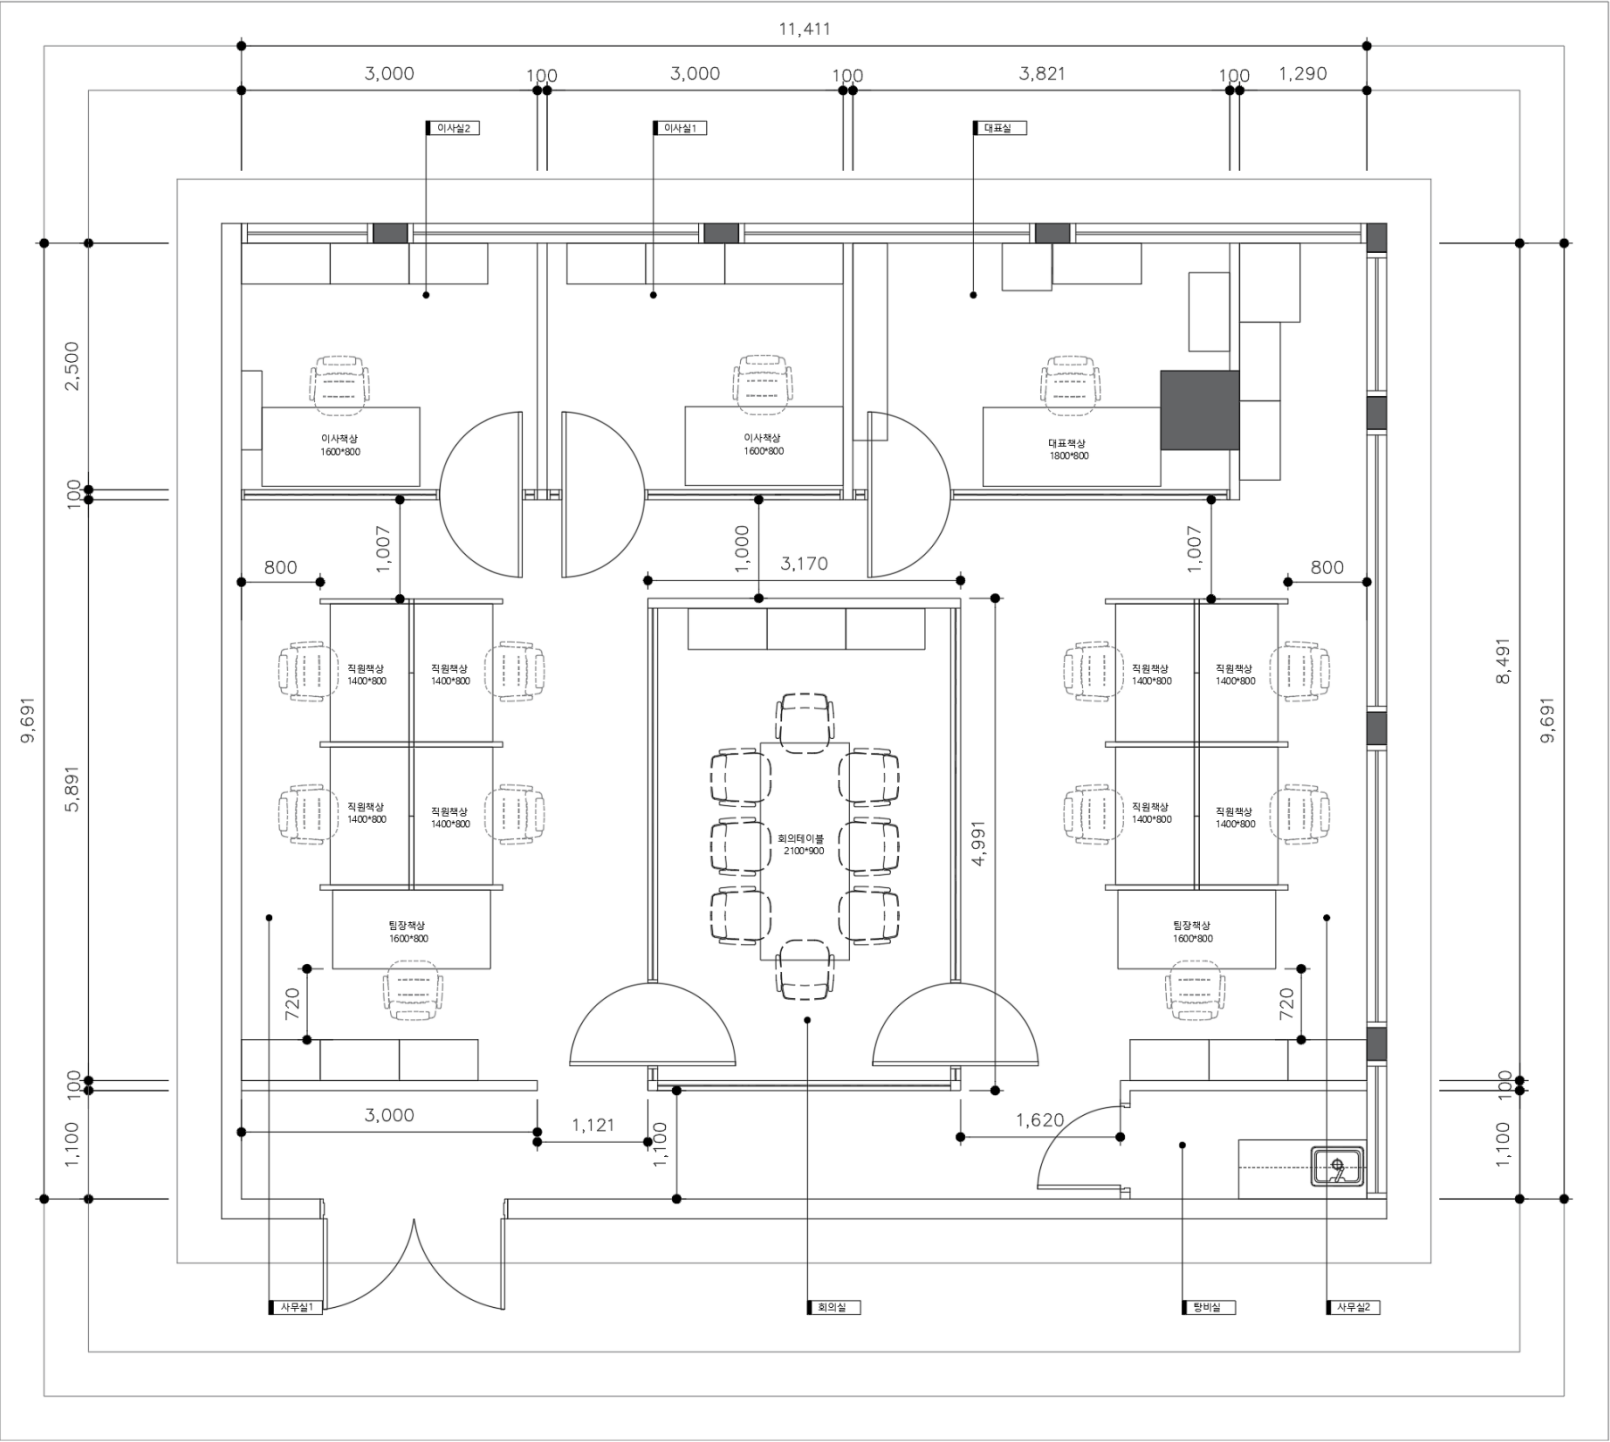

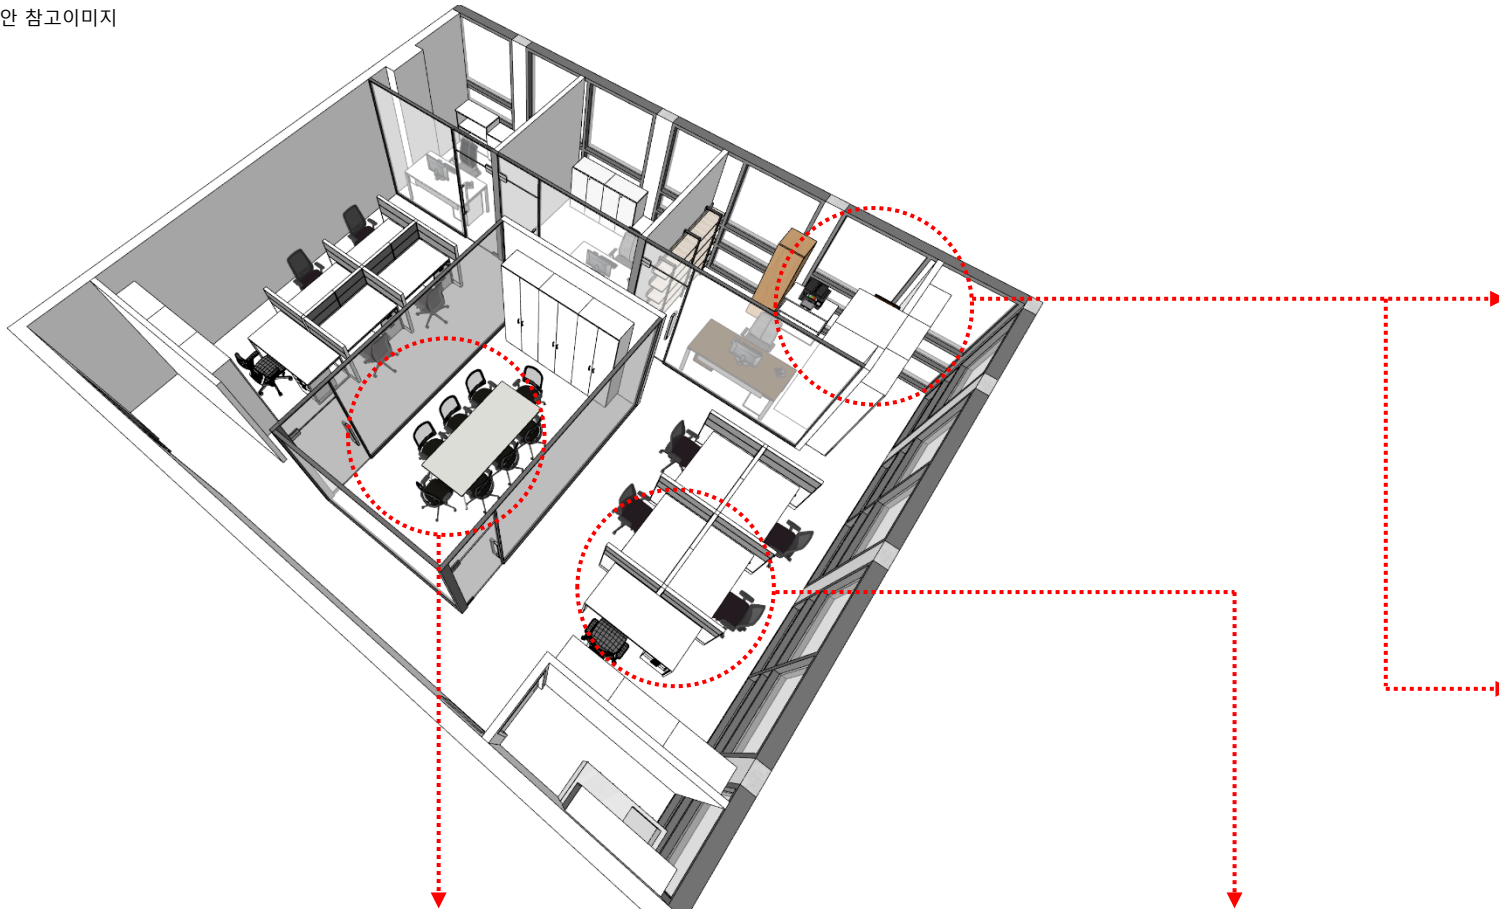

대표실 및 이사실



대표실 및 이사실





회의실



사무실

평면도

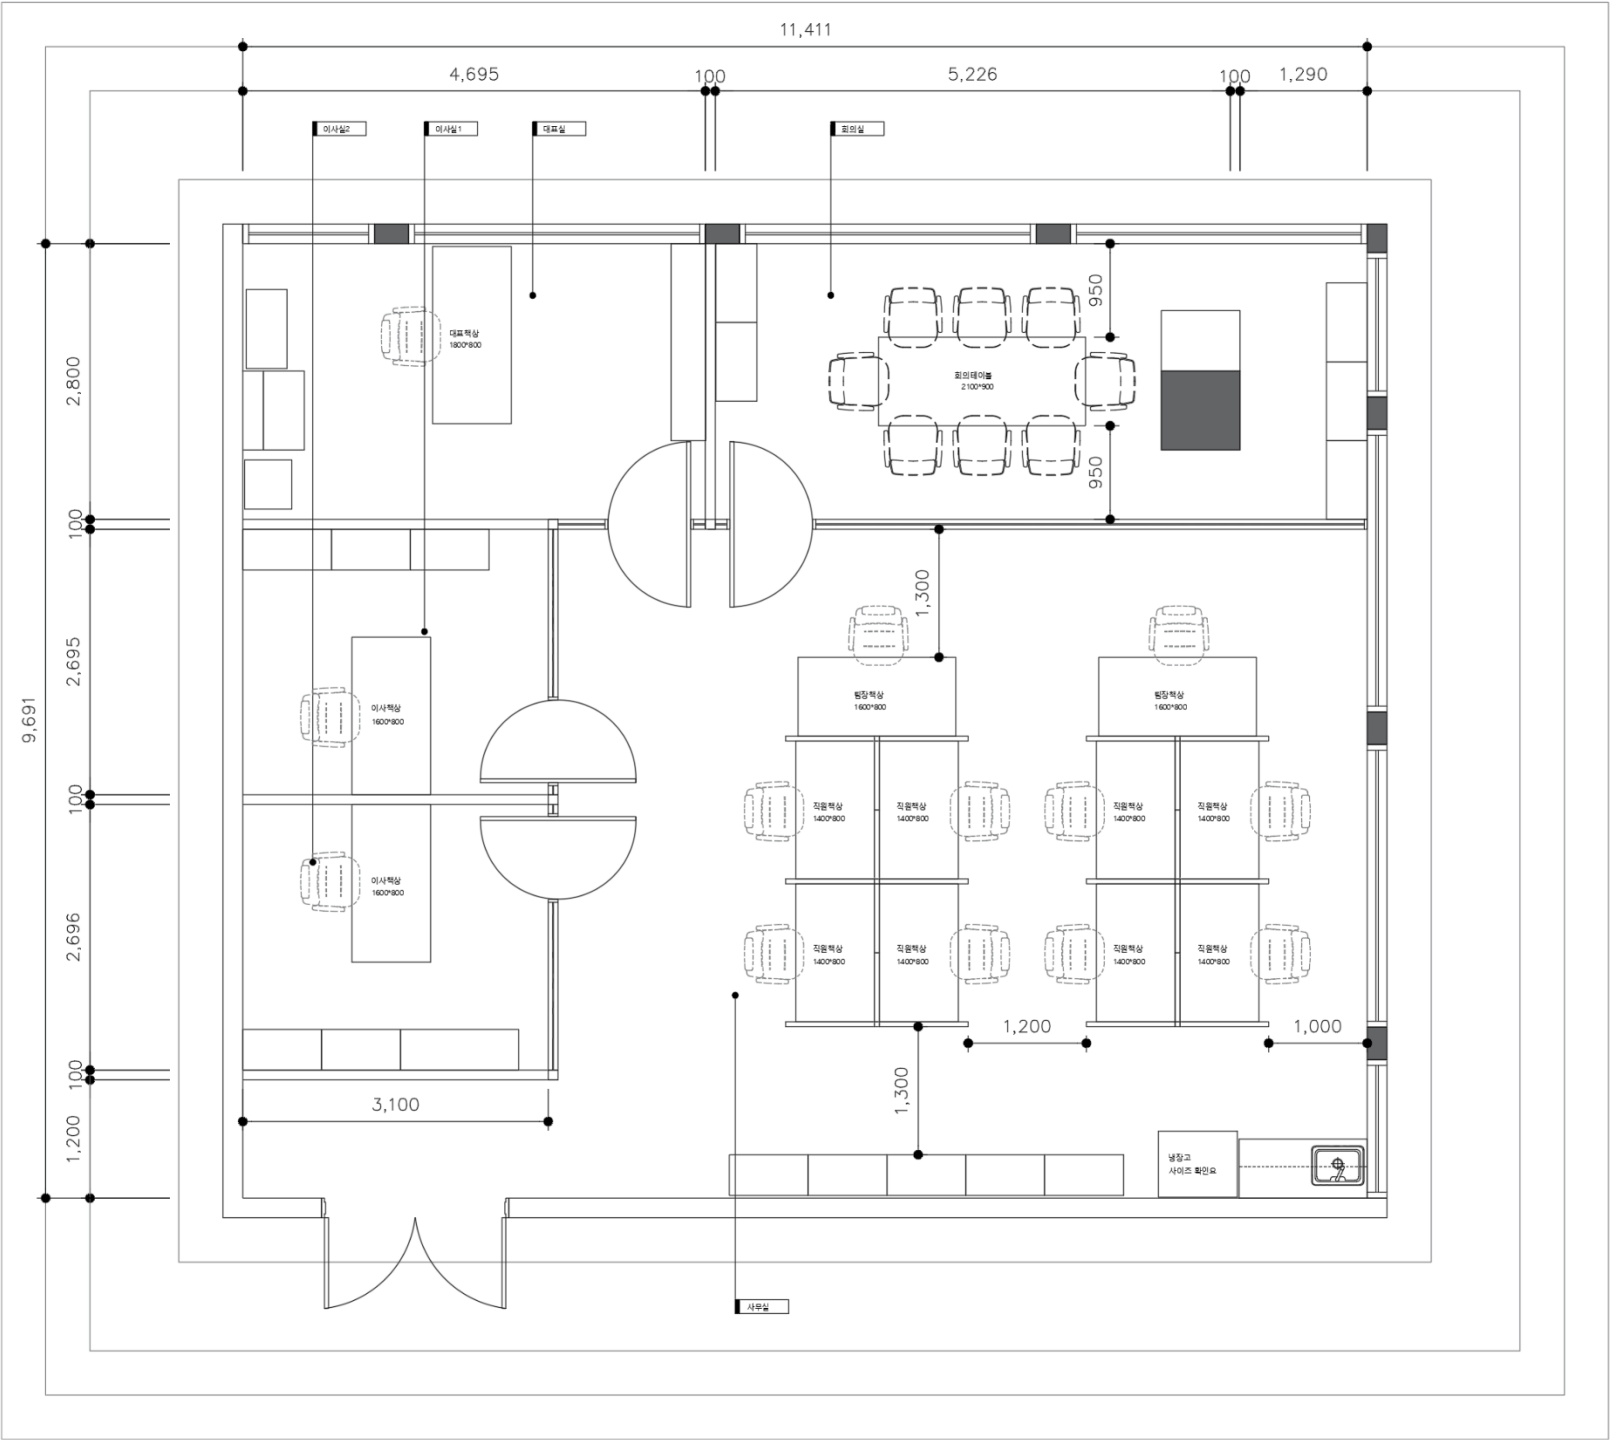

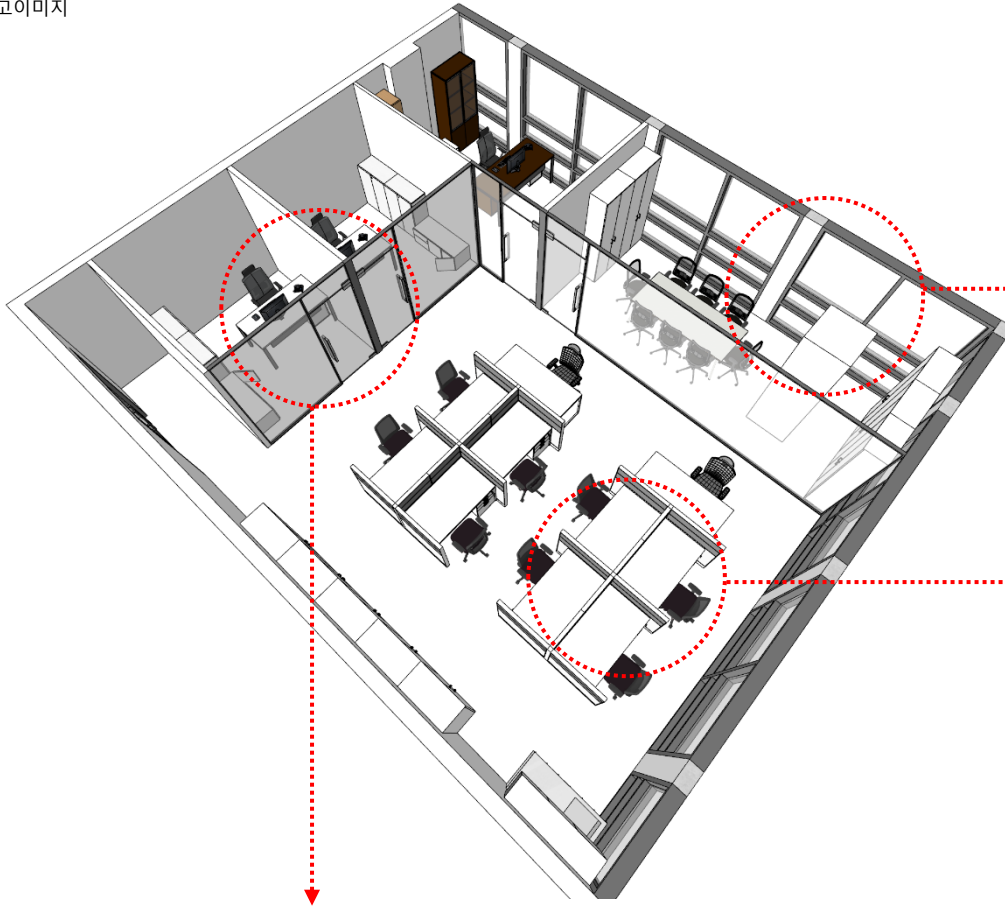

회의실



사무실



대표실 및 이사실





대표실 및 이사실



사무실

평면도

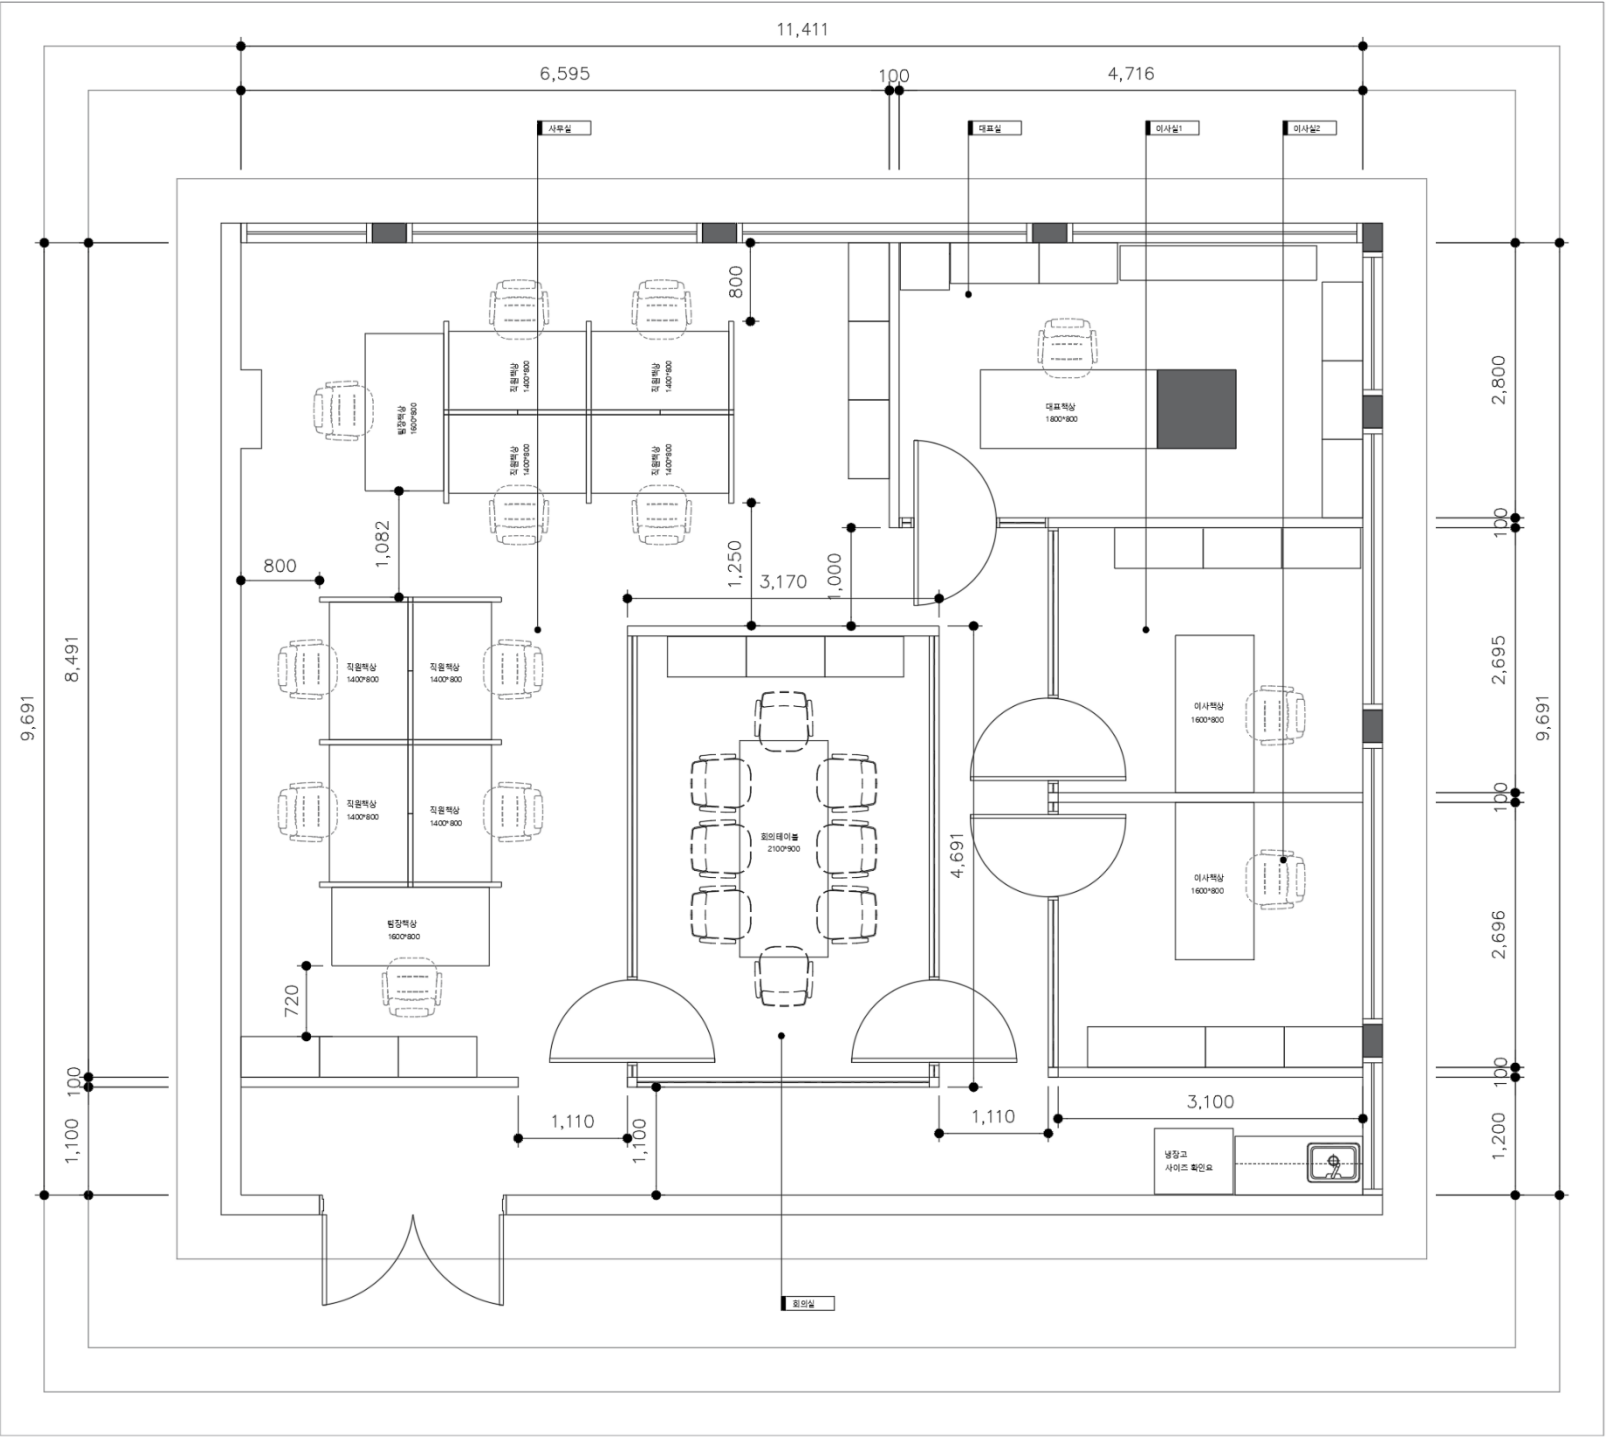

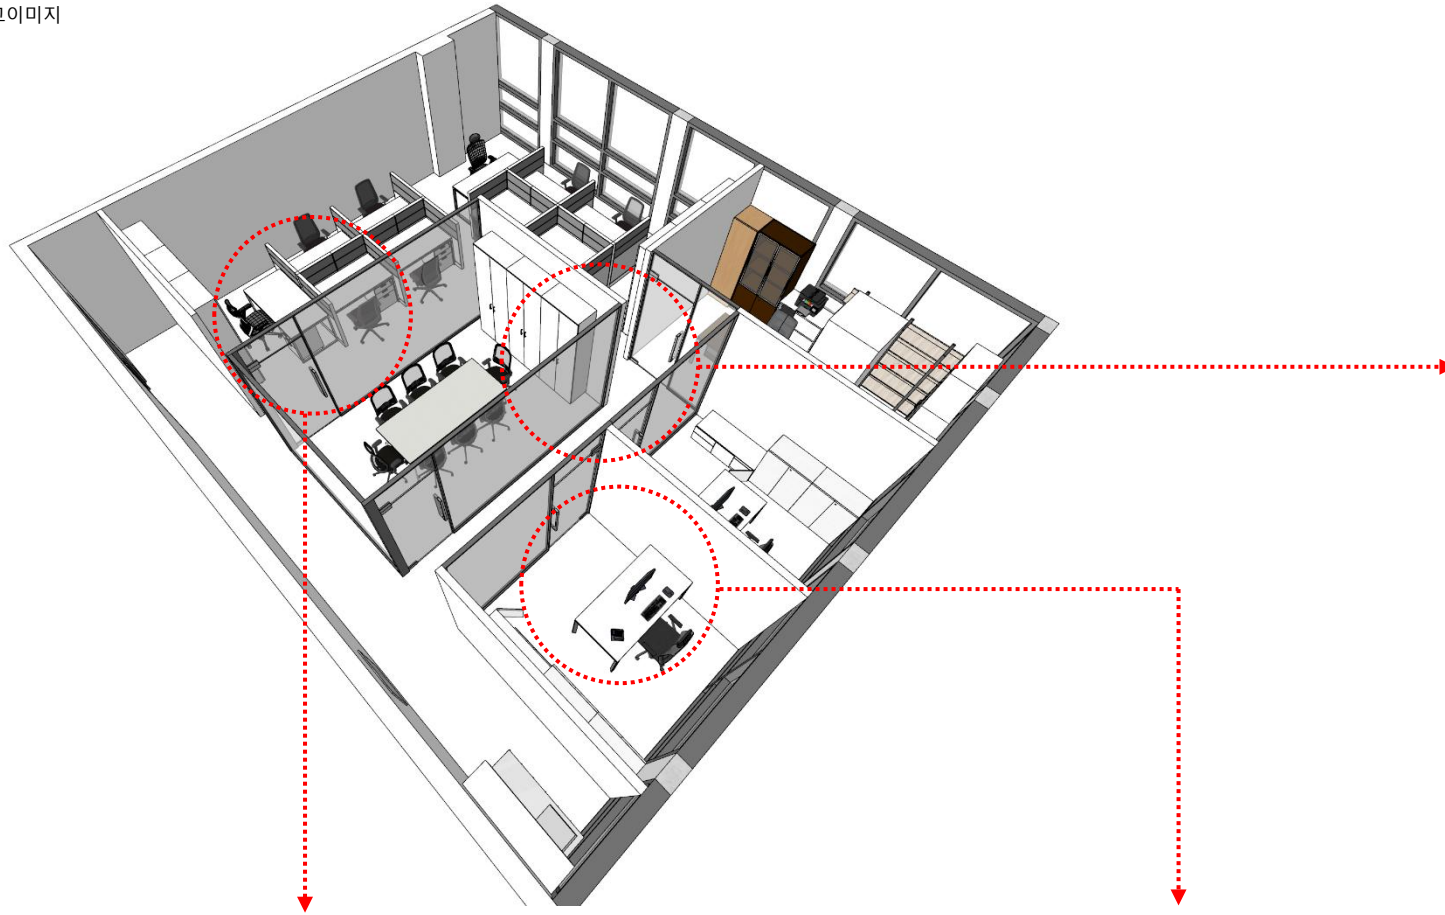

사무실 및 회의실



이사실

사무실 및 복도